


R+1

60x120 TONALITY CHAMPAGNE NAT  
 plinthe bois (hors lot)  
 Joint Gris ciment  
 Joint aligne' - SENS POSE

— faïences

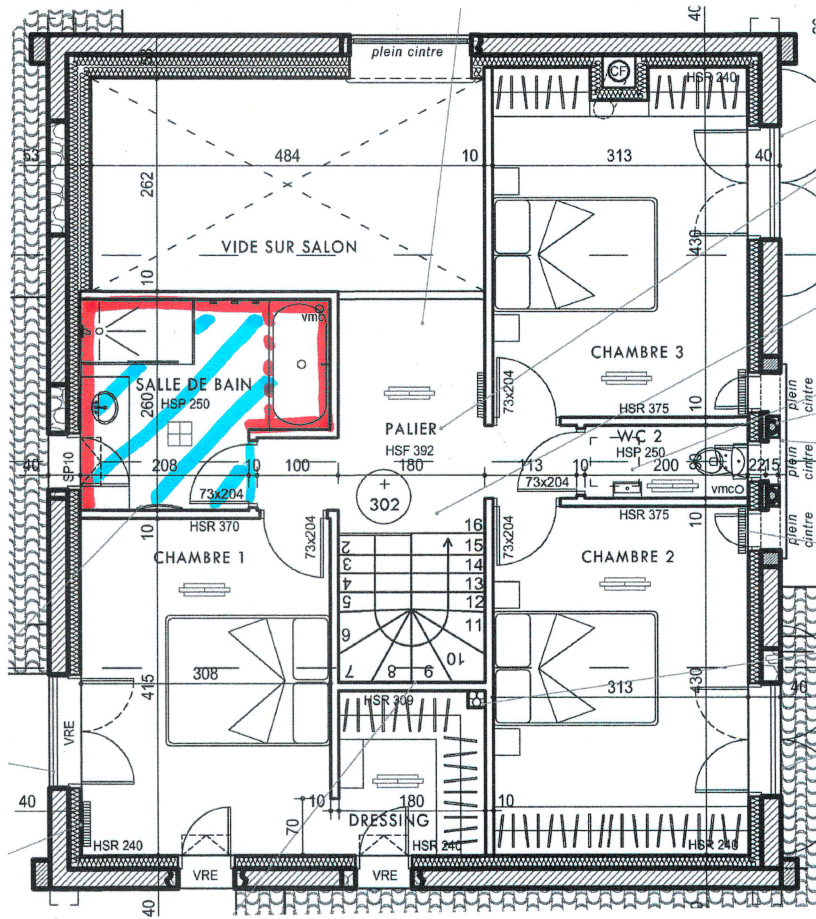


LORIGER. ROUILLARD

RDC

60x60 LITHOS TORTORA + PL  
 Joint Gris Ciment

— faïences

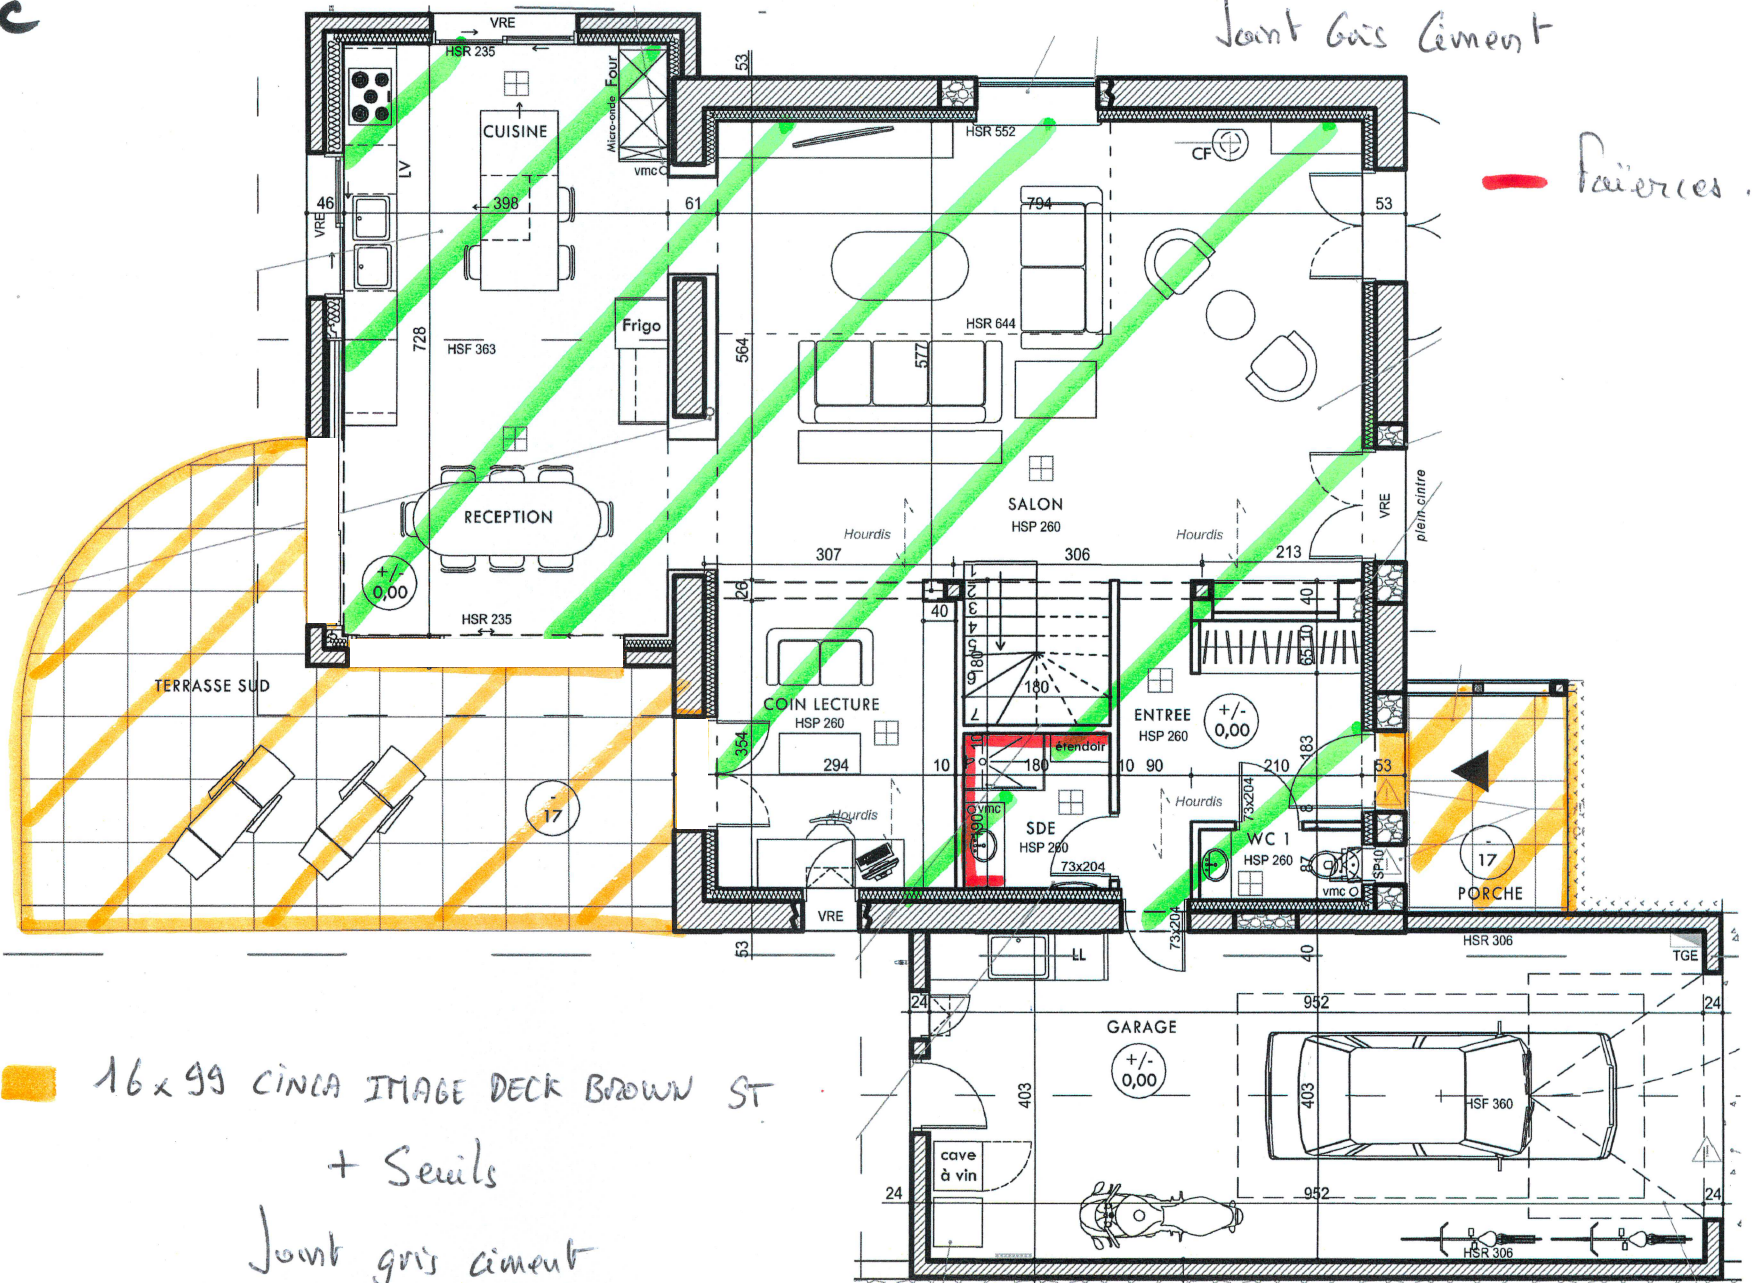


16x99 CINCA IMAGE DECK BROWN ST  
 + Seuils

Joint gris ciment

Pose à joint Perdu sens pose


- 20x40 CINCA ARQUITECTOS CLEMENTINE BR 2288
- 10x30 CINCA ARQUITECTOS CLEMENTINE BR 2288
- 40x120 RAGNO RESINA BIANCO R79U
- 40x120 RAGNO RESINA décor BIANCO STRUTTURA 3D WALL R79E

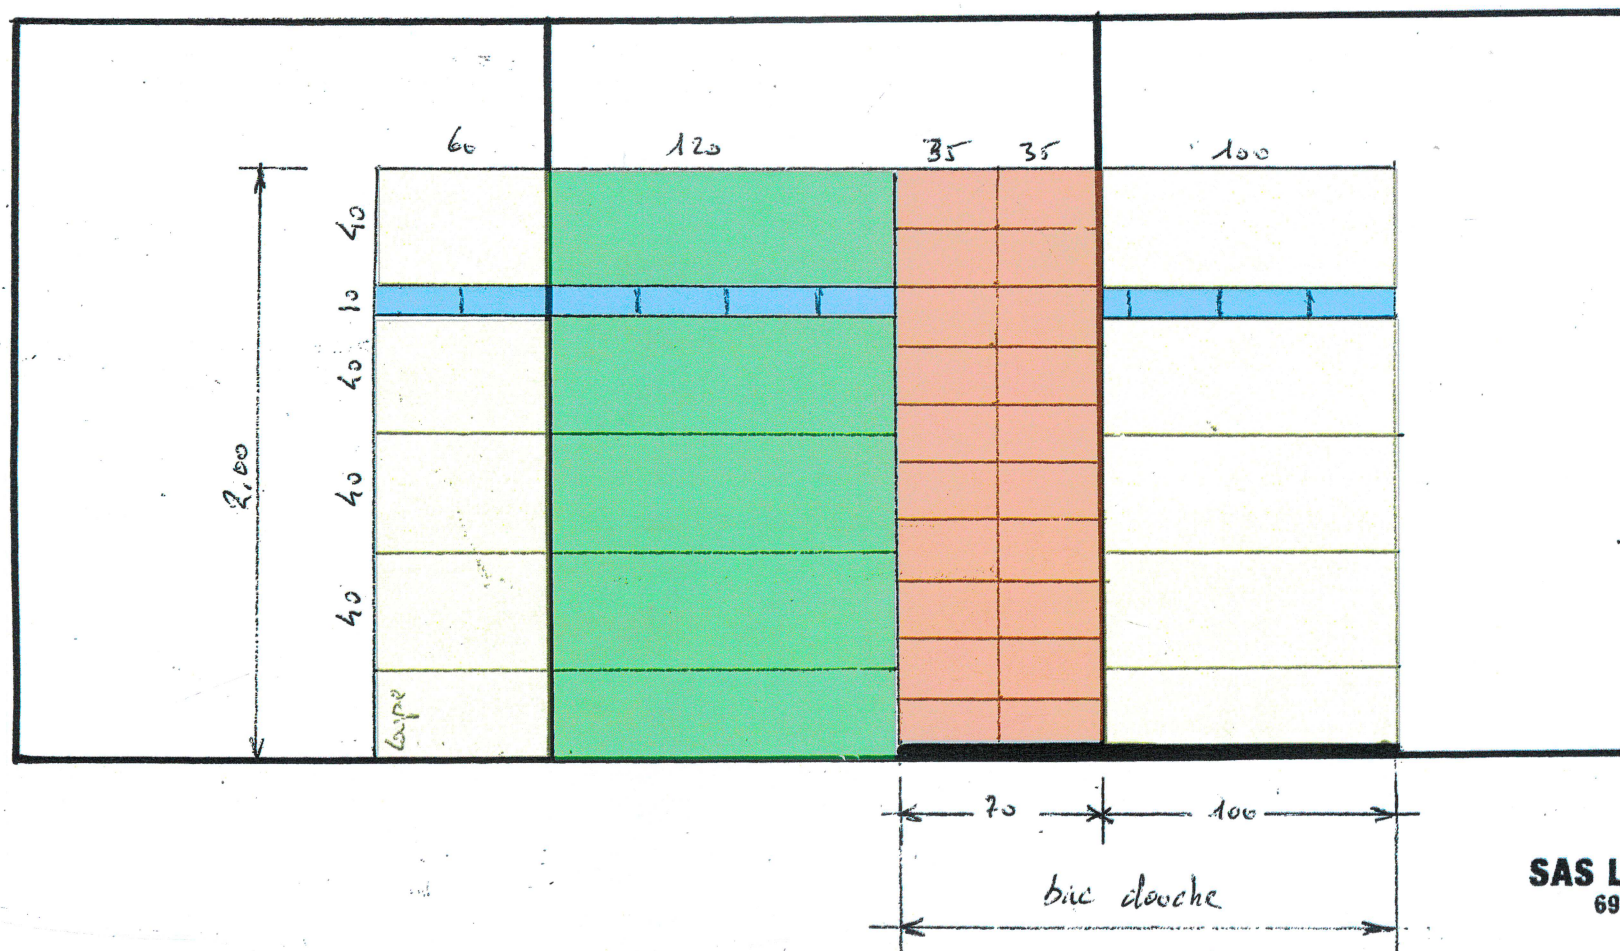

SDE - RDC

**SAS LESCA CARRELAGE**  
 699, Route de Condrette  
 40400 TARTAS  
 Tél. : 05 58 73 46 19  
 Mail : s.lesca@bernadet.net  
 SIRET : 341 924 546 00011

POSE HORIZONTALE - HAUTEUR 2,00 m  
 Joint Blanc + bg AR ALU

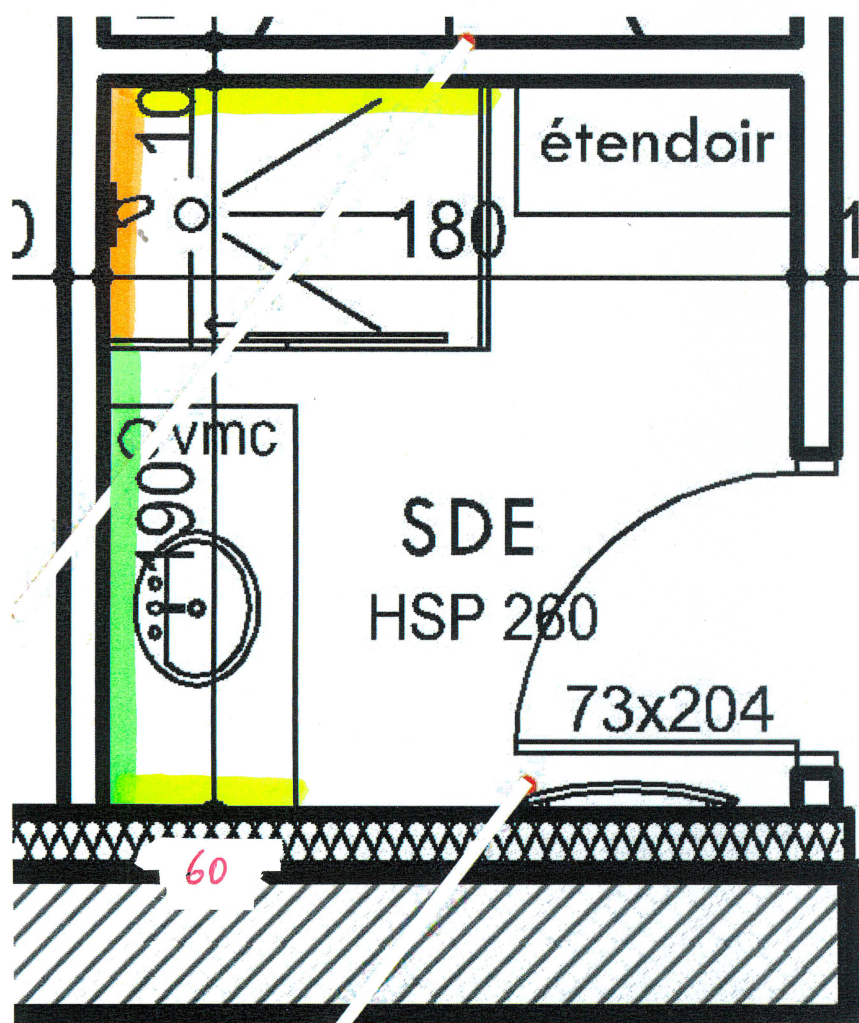

SDE - RDC

- 40x120 RAGNO RESINA BIANCO R79U  
 + Frise 10x30 CINCA CLEMENTINE GLOSSY 2288  
 SUIVANT CALEPINAGE
- 40x120 RAGNO RESINA décor BIANCO STRUTTURA 3D WALL R79E  
 + Frise 10x30 CINCA CLEMENTINE GLOSSY 2288
- 20x40 CINCA ARQUITECTOS CLEMENTINE GLOSSY 2288  
 PAS DE FRISE  
 SUIVANT CALEPINAGE